Floor plan

10 x 10 m clear · 8 buttresses · printed walls


1. Printed wall 400 (= ring beam width = roof base width). Buttresses solid black: 400 wide (same as the wall), 700 deep from the inner face (flush with the wall inside), so they project 300 outside.
2. Openings, one per bay between the buttresses: doors 1000 (south-west and north-east bays), windows 1800 in the other six. Positions and sizes are placeholders.
3. Pyramid roof above (dashed): 1000 square crown, hips to the corners, roof base 400 thick square to the slope, so its outer edge lands about 59 outside the wall face.
4. Buttresses at the 4 corners and the 4 mid-spans, axes 5200 apart (centre to centre of wall).

● from your sketches
○ assumed by me, to confirm

Notes

Section A-A cuts through the east and west mid-span buttresses.

Detail D1 is the eave at the east mid-span buttress.

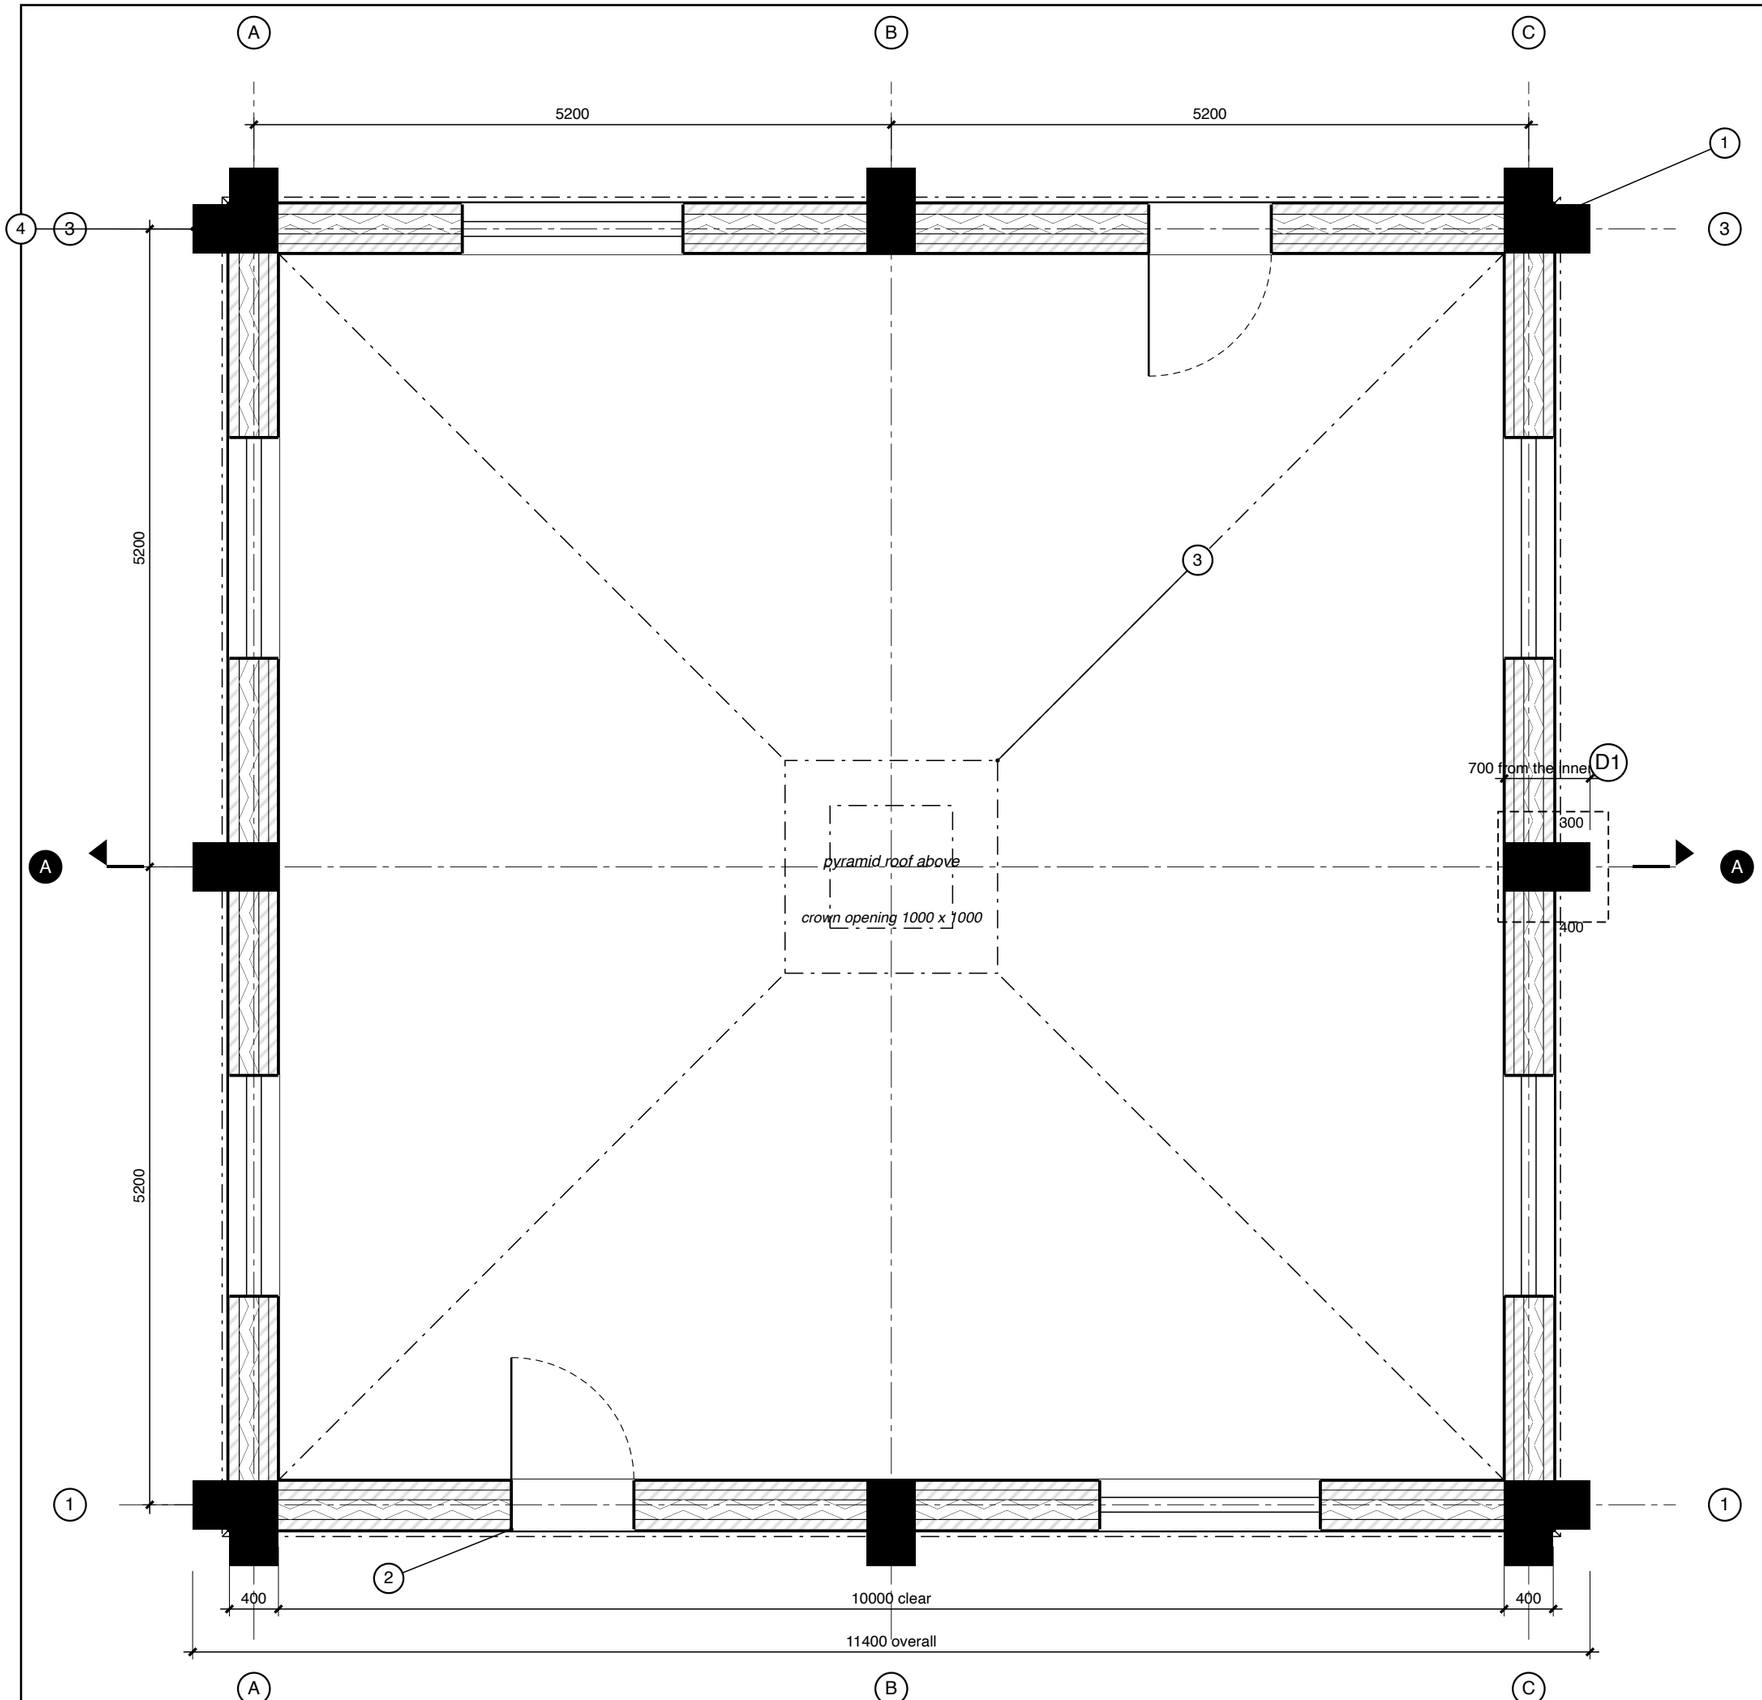

0 1 2 3 4 5 m

Scale 1:50 at A3 · dimensions in mm · draft 1, 2026-10-11
pyramid-roof · hand estimates, not engineered