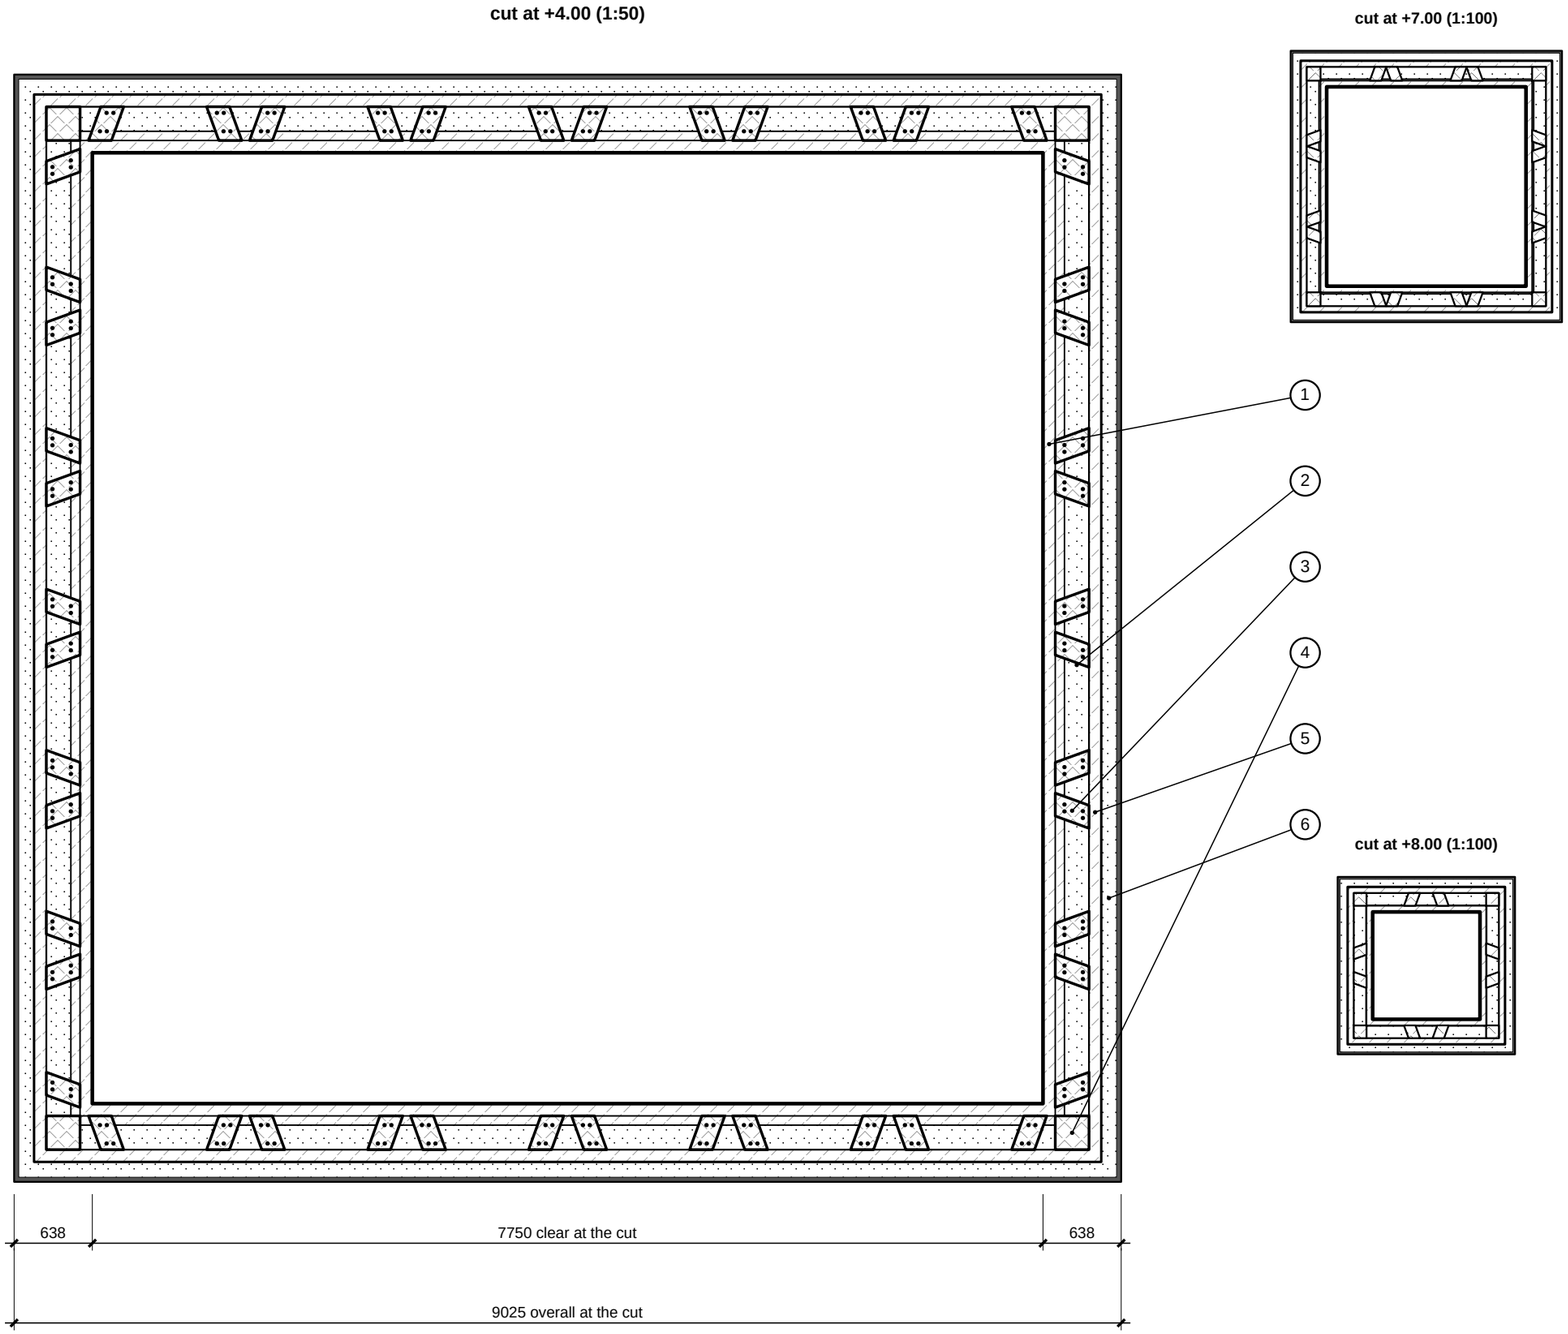


Roof plan slices · grid B

horizontal cuts through the roof, looking down

1. Inner layer 1, 80 printed, room side, then layer 2 (printed, thinner towards the crown).
2. Air zone, open between the ribs, for insulation (dotted).
3. Cast ribs cut by the plane (crossed hatch): the two diagonal families of grid B; each 160 wide across the rib and 240 deep. The cut is longer than 160 and sheared where the rib is inclined in the face; 4 Ø16 and stirrups as in the rib section.
4. Corner blocks: the four hip ribs, cut across the corners (cast).
5. Outer layer 80, printed.
6. Insulation 100 (very thin line), then the outer layer 30 (dark).

● from your sketches
○ assumed by me, to confirm

Notes

Large slice at +4.00 (1500 above the eave), 1:50; small slices at +7.00 and +8.00, 1:100.

Option B: the same two diagonal families at every height; the cut ribs move towards the corners as the roof narrows, the diamonds are clipped by the hips.

Layer 2 thins towards the crown (the leaf is 160 at the base, 80 at the crown). Ribs use the same geometry as the roof-grid sheets; bars and stirrups are assumed.

0 1 2 3 4 5 m

Scale 1:50 at A3 · dimensions in mm · draft 1, 2026-10-11
pyramid-roof · hand estimates, not engineered