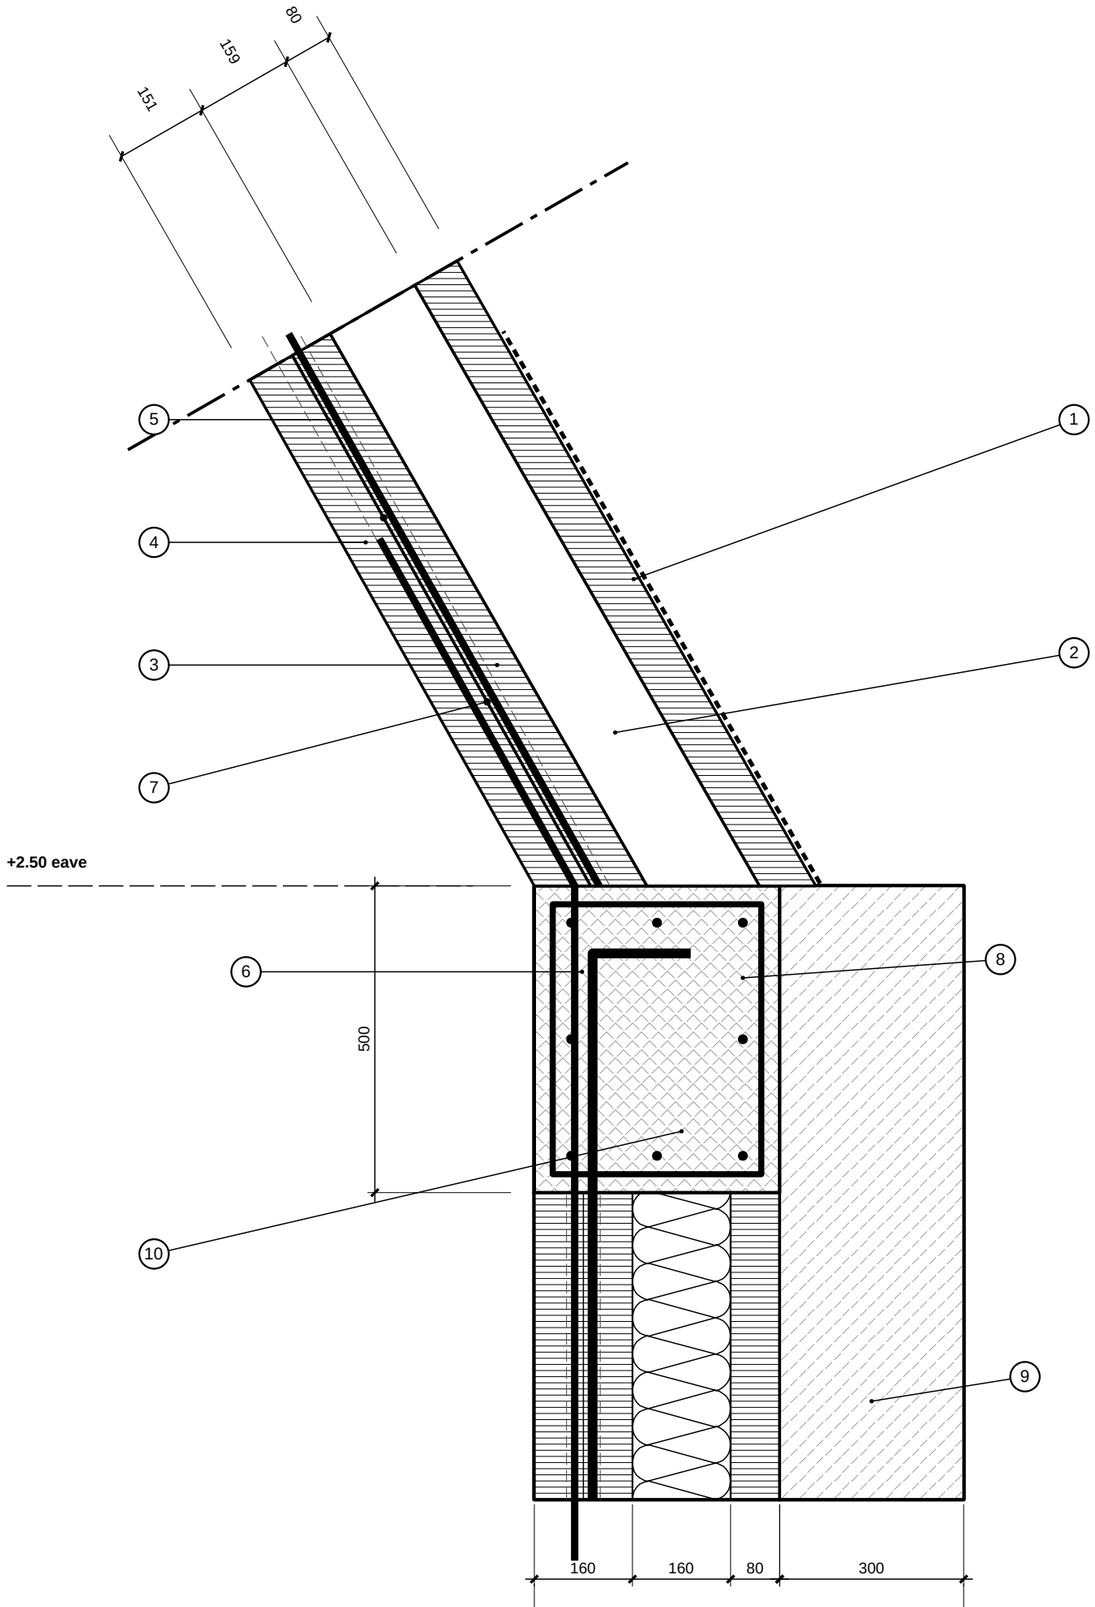

Plan of one roof piece, 1:5

layer pattern, bars every @ 600 along the path

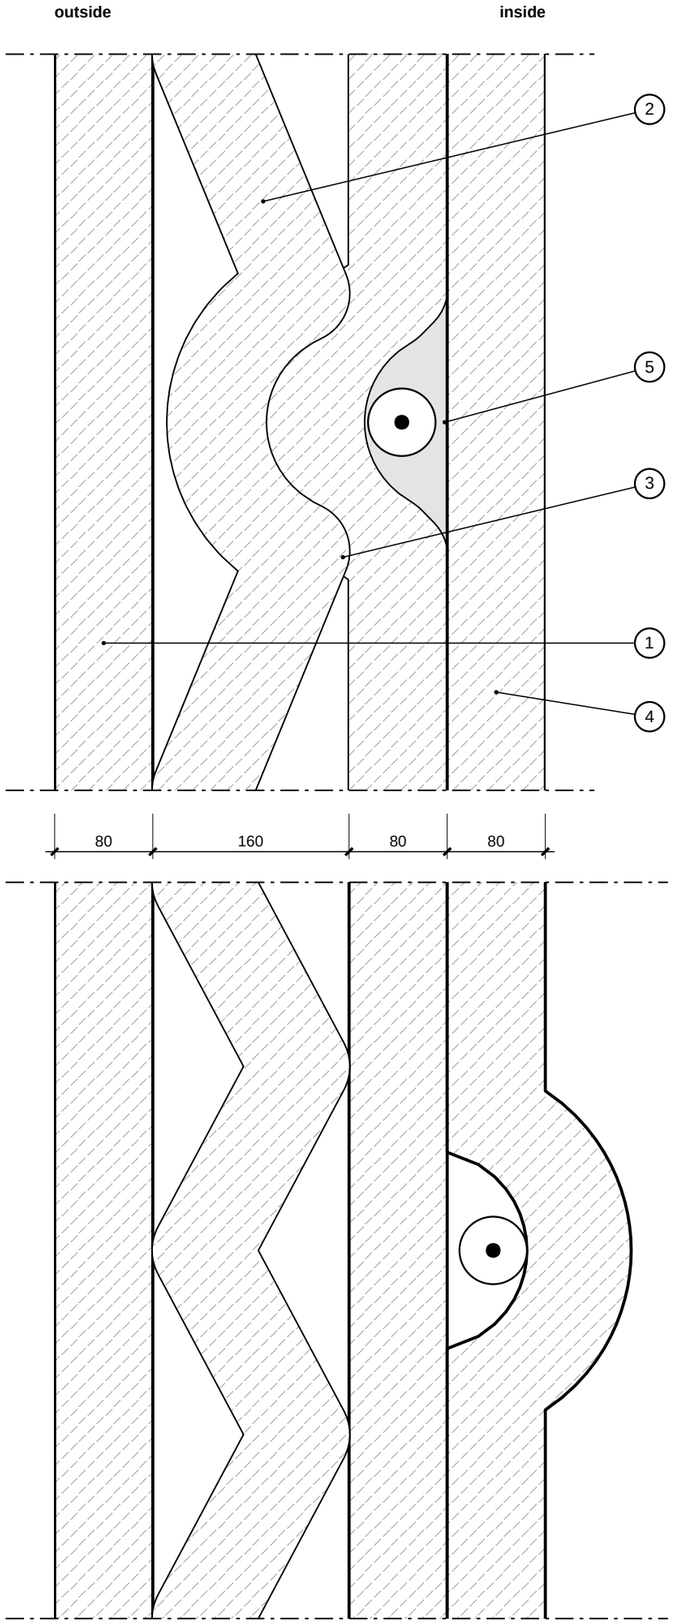

Detail D1: eave, roof to wall

1. Roof outer layer 80, printed with the rest of the piece; cladding on the outside face (dashed line).
2. Zig-zag lattice 80 in a 160 zone; it touches the outer layer and layer 2 every @ 600; the cells between are open air pockets for ventilation.
3. Layer 2, 80: printed bead that curves to leave a pocket for the bar.
4. Inner layer 1, 80, room side. Layers 1 and 2 together are the structural leaf: 160 at the base, 80 at the crown (layer 2 ends).
5. Rebar pocket Ø55 in the leaf, grouted after placing. Roof bars R Ø12 every @ 600 along the path.
6. Knee bars B Ø12 every @ 600, one continuous bar over the eave: 1100 down the wall pocket (laps wall bars A), through the beam, 650 up the roof.
7. Ring bars Ø12 in the pocket zone every 300.
8. Ring beam 400 x 500, cast in place: 8 Ø16, closed stirrups Ø10 / 150; wall bars A hook into it. Embedded in the buttress notch.
9. Buttress 400 wide, 1000 from the inner face (600 beyond the wall), L-shaped around the ring beam; top flush with the roof base at +2.50.
10. Wall 400 printed, same pattern as the roof; wall bars A Ø16 run from the footing up into the beam and end in a 160 hook (assumed).

● from your sketches
○ assumed by me, to confirm

0 1 2 3 4 5 dm

Scale 1:10 at A3 · dimensions in mm · draft 1, 2026-10-11
pyramid-roof · hand estimates, not engineered